

BETECKNINGAR

LED 1 (FUNKTION)

T = TILLUFT
F = FRÄNLUFT
U = UTELUFT
A = AVLUFT
Ö = ÖVERLUFT

LED 2 (MATERIAL)

1 = FÖRZINKAD STÅLPLÅT
6 = FLEXIBEL KANAL (SLANG)

LED 3 (ISOLERUTFÖRANDE)

B101 = UTV ISOL. E15 NÄTMATTA
B103 = UTV ISOL. E130 NÄTMATTA
B106 = UTV ISOL. E160 NÄTMATTA
B201 = UTV ISOL. E15 NÄTMATTA MED AL-FOLIE
B203 = UTV ISOL. E130 NÄTMATTA MED AL-FOLIE
B206 = UTV ISOL. E160 NÄTMATTA MED AL-FOLIE
V103 = UTV ISOL. VÄRME 30 MM NÄTMATTA
V105 = UTV ISOL. VÄRME 50 MM NÄTMATTA
V106 = UTV ISOL. VÄRME 60 MM NÄTMATTA
V107 = UTV ISOL. VÄRME 70 MM NÄTMATTA
V108 = UTV ISOL. VÄRME 80 MM NÄTMATTA
K719 = UTV ISOL. KONDENS CELLGUMMI 19 MM

FÖRKLARINGAR

LUFTMÄNGDER ANGIVNA I l/s
MIN 100 mm MELLAN INGJUTNA KANALER
KANALDIM = 125 mm DÄR EJ ANNET ANGES
KORTBÖJAR ANVÄNDS DÄR SÅ ERFORDRAS

SP201 = INJUSTERINGSSPJÄLL TYP IRISSPJÄLL
SP701 = REKTANGULÄRT AVSTÄNGNINGSSPJÄLL
SP702 = REKTANGULÄRT AVSTÄNGNINGSSPJÄLL
BSS101 = SJÄLVVERKANDE BACKSTRÖMNINGSSKYDD
LD101 = CIRKULÄR LUDDÄMPARE
LD201 = LJUDDÄMPARE FÖR TYP CADENZA
LD401 = LJUDDÄMPARE FÖR TYP LENTO
TD201 = TILLUFTSDON FÖR TAK CTVB
TD202 = TILLUFTSDON FÖR TAK KE
FD101 = FRÄNLUFTSDON KONTROLLVENTIL
SF701 = SPISFLÄKT
SLA101 = SAMLINGSLÅDA FÖR FRÄNLUFT
SLA102 = FÖRDELNINGSLÅDA FÖR TILLUFT

B V-PM2 220121 VN
A V-PM1 211119 VN

BET ANDRINGEN AVSER DATUM SIGN

BYGGHANDLING

NCC LAMELL 2021




SJÖMÄRKET 1
VÄSTERÅS

A	Arkinova Arkitekter	tel. 090-15 98 50
K	NCC Teknik och Hållbarhet	tel. 08-585 510 00
L	VAP VA-PROJEKT AB	tel. 019-17 52 55
X	V Ramböll	tel. 010-615 49 44
VS	Ramböll	tel. 010-615 49 44
E	ELTE Konsult	tel. 090-13 73 30
Br	NCC Teknik och Hållbarhet	tel. 08-585 510 00
		tel. -


UPPDRAG NR 1320055999	RITAD/PROJEKT. AV E. HÖGLUND	HANDLÄGGARE V. NILSSON
DATUM 2021-11-19	ANSVARIG VICTOR NILSSON	

LUFTBEHANDLING
PLAN 10 - DEL 4

SKALA A1 1:50 A3 1:100	NUMMER V-57-1-1104	BET B
------------------------------	-----------------------	----------

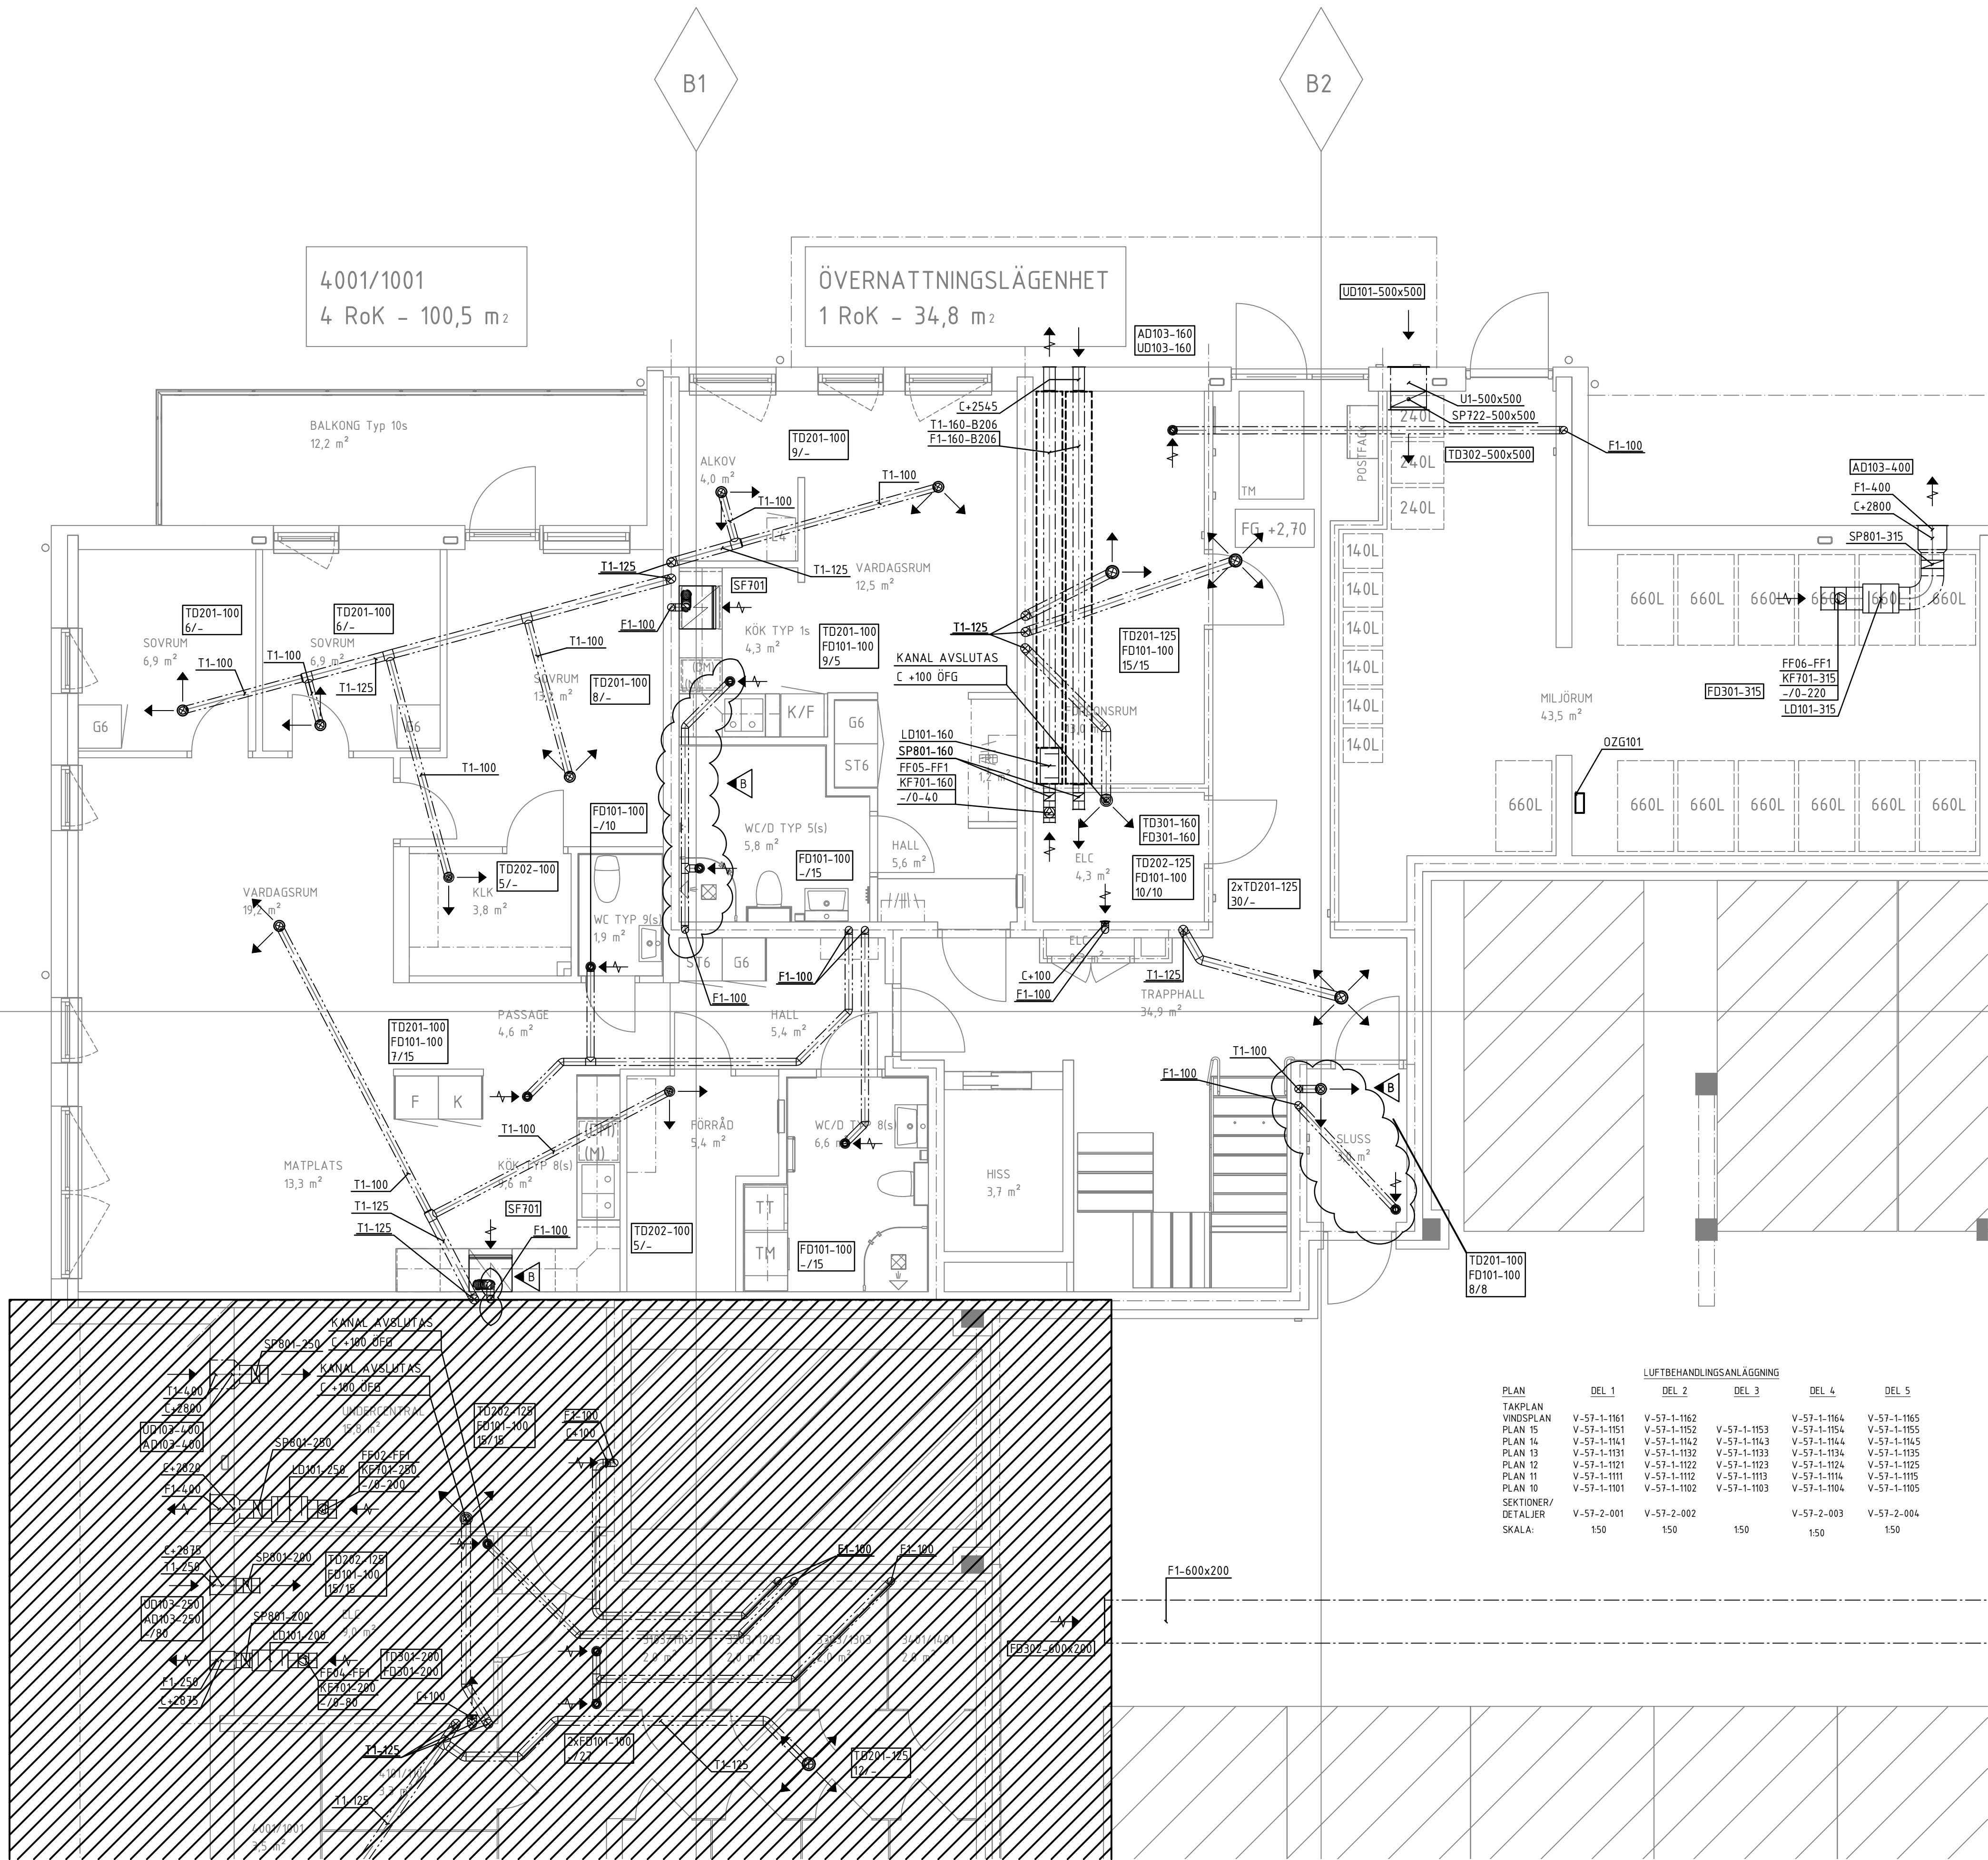

SKALA 1:50

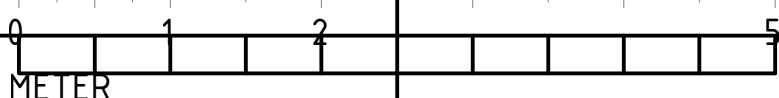

PLAN	DEL 1	DEL 2	DEL 3	DEL 4	DEL 5
TAKPLAN					
VINDSPLAN	V-57-1-1161	V-57-1-1162		V-57-1-1164	V-57-1-1165
PLAN 15	V-57-1-1151	V-57-1-1152	V-57-1-1153	V-57-1-1154	V-57-1-1155
PLAN 14	V-57-1-1141	V-57-1-1142	V-57-1-1143	V-57-1-1144	V-57-1-1145
PLAN 13	V-57-1-1131	V-57-1-1132	V-57-1-1133	V-57-1-1134	V-57-1-1135
PLAN 12	V-57-1-1121	V-57-1-1122	V-57-1-1123	V-57-1-1124	V-57-1-1125
PLAN 11	V-57-1-1111	V-57-1-1112	V-57-1-1113	V-57-1-1114	V-57-1-1115
PLAN 10	V-57-1-1101	V-57-1-1102	V-57-1-1103	V-57-1-1104	V-57-1-1105
SEKTIONER/ DETALJER	V-57-2-001	V-57-2-002		V-57-2-003	V-57-2-004
SKALA:	150	150	150	150	150

