


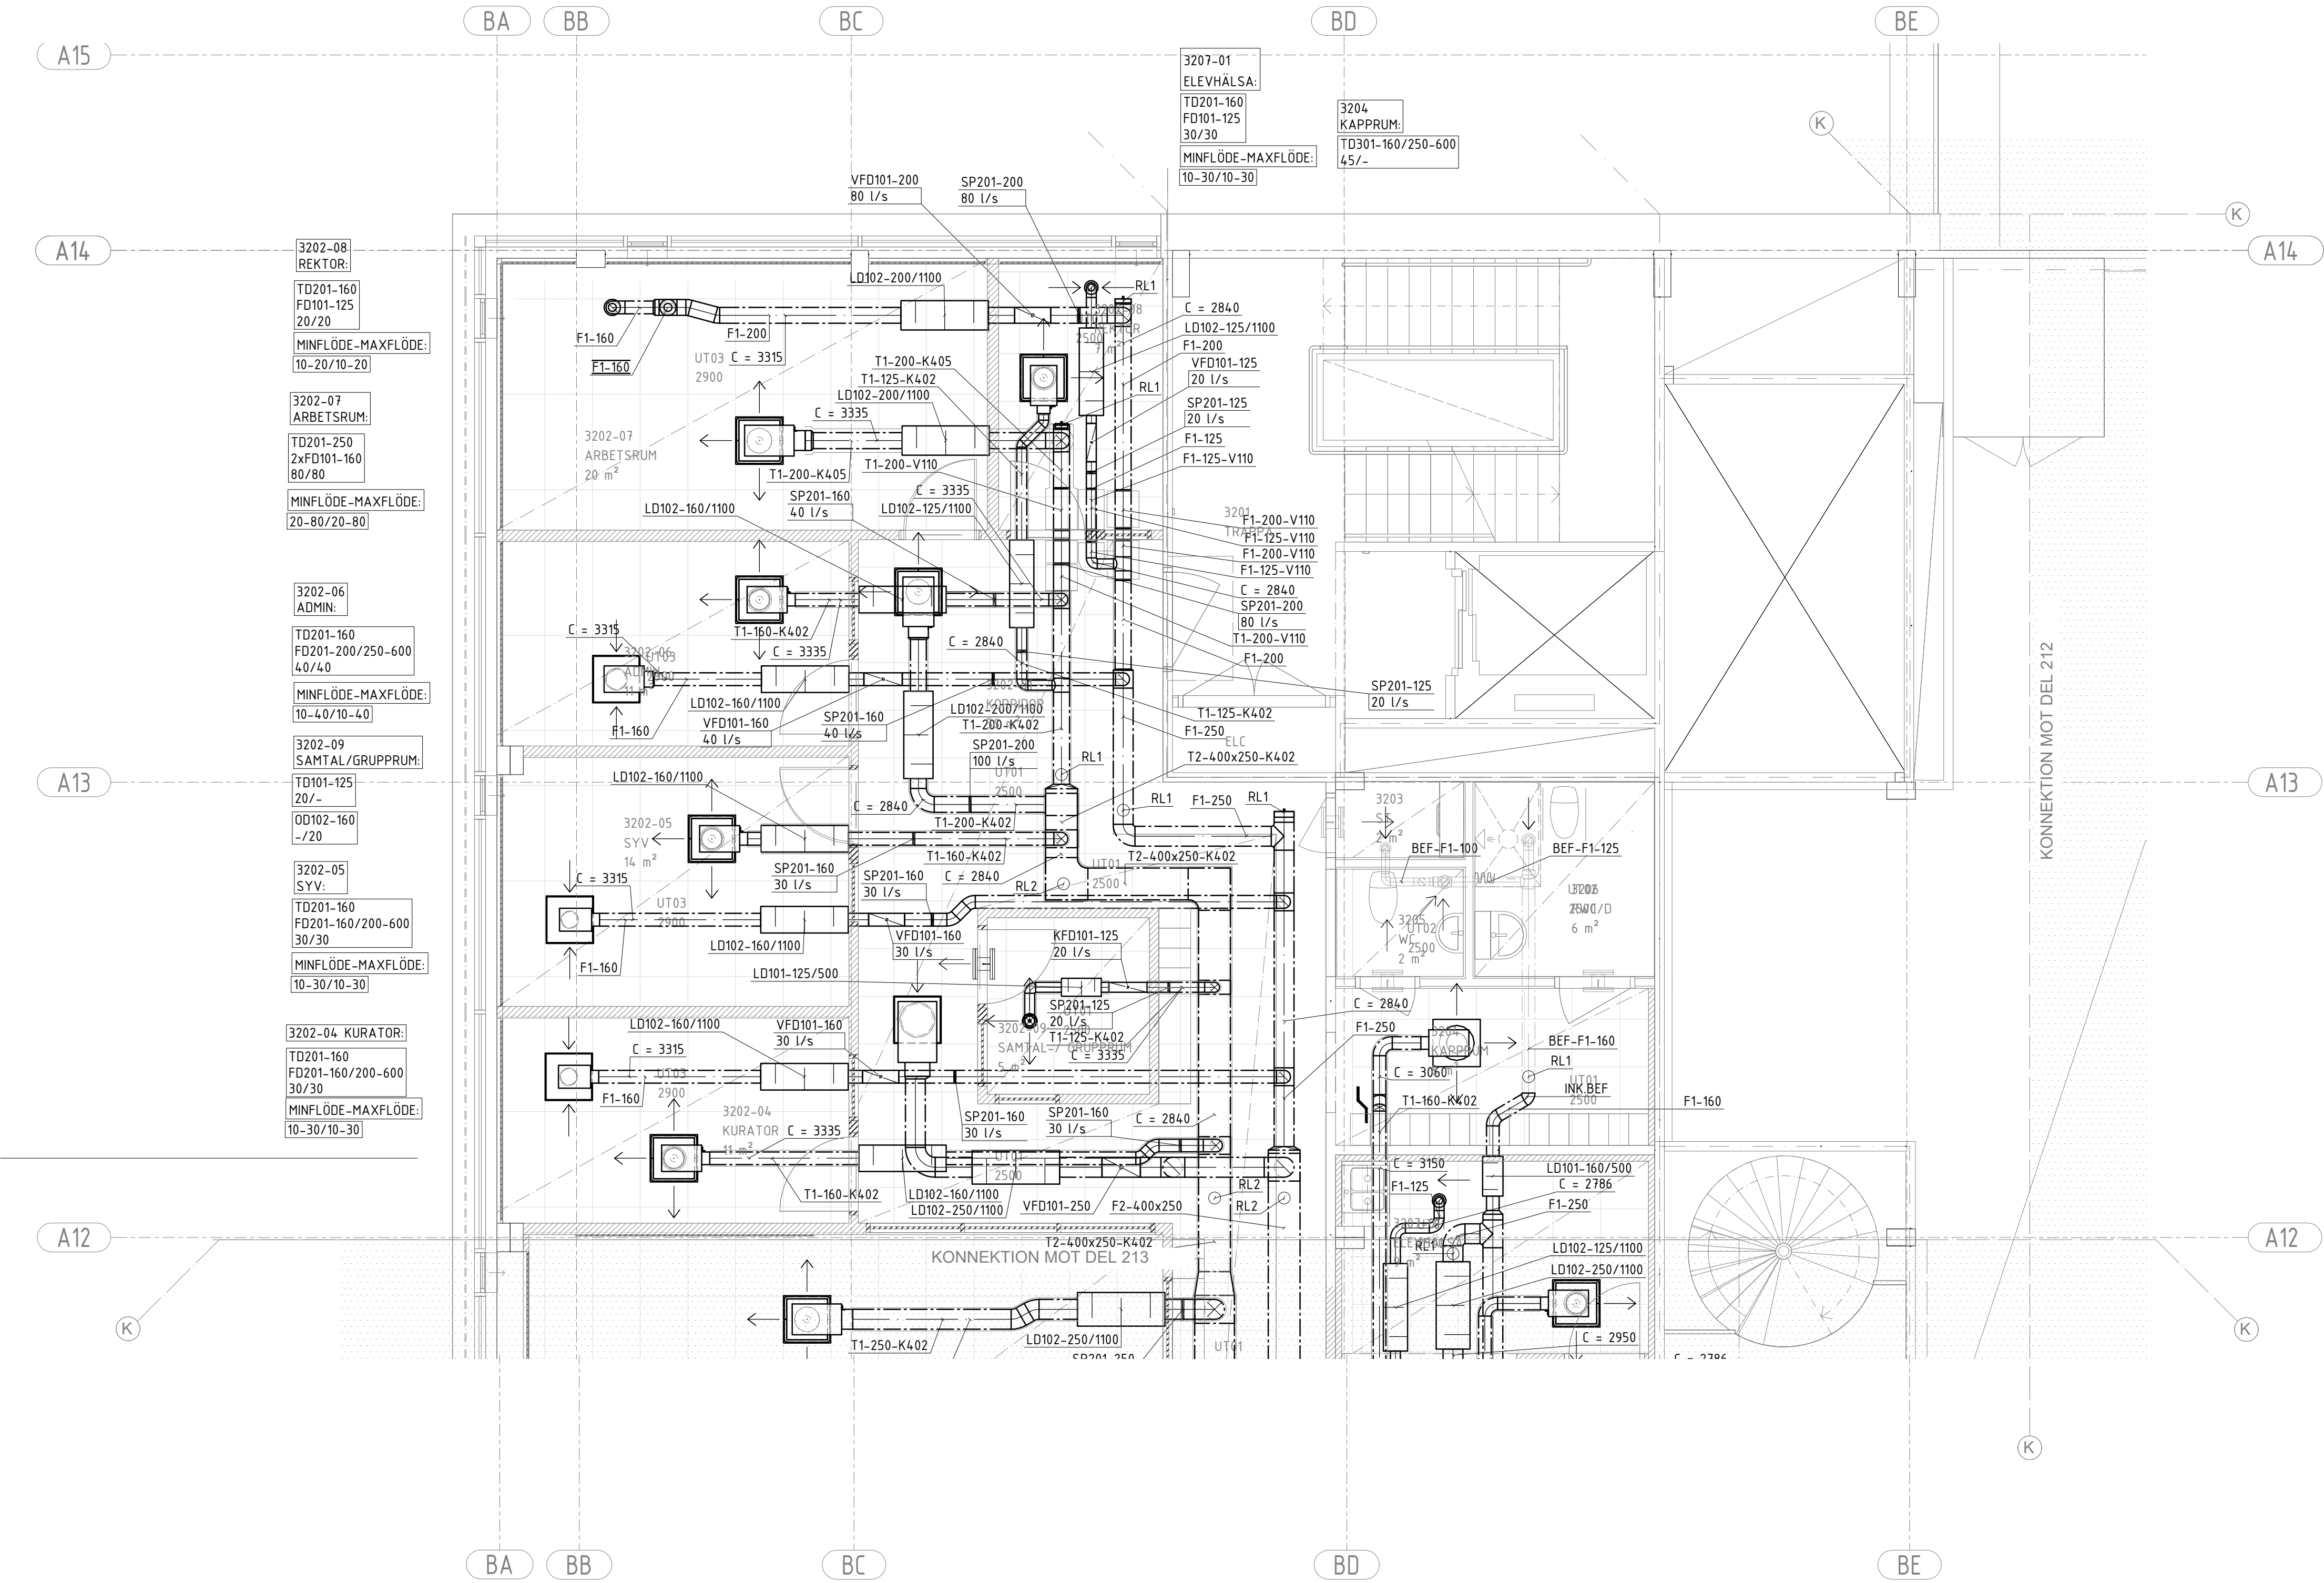

FÖRKLARINGAR

SYSTEM
T TILLUFT
F FRÅNLUFT
U UTELUFT
A AVLUF
Ø OVERLUFT

KANALMATERIAL:

1 CIRKULÄRA KANALER, VÄRMFÖRZINKADE.
2 REKTANGULÄRA KANALER, VÄRMFÖRZINKADE.

ISOLERING:

K402 KONDENSISOLERING, 20 mm.
K405 KONDENSISOLERING, 50 mm.
V110 VÄRMEISOLERING, 100 mm.
B106 BRANDISOLERING, UTV. NÄTMATTA, E160

SAKVAROR:

LD101 CIRKULÄR LJUDDÄMPARE, SWEGON SORDO-A E130.
LD102 CIRKULÄR LJUDDÄMPARE MED BAFFEL, SWEGON SORDO-C E160.
LD201 REKTANGULÄR LJUDDÄMPARE, SWEGON CADENZA.
SP201 IRISSPJÄLL.
VFD101 VARIABELFLÖDESDON, CIRKULÄRT, SWEGON, WISE DAMPER.
KFD101 KONSTANFLÖDESDON, CIRKULÄRT, SWEGON, WISE DAMPER.
BBS101 BRAND/BRANDGASSP. (CIRK. BEVENT RASCH, BSKC6.
BBS102 BRAND/BRANDGASSP. (REKT. BEVENT RASCH, BSKC6.

LA012

TILLUFTSDON, FLÄKT WOODS STI-C.
AKTIVT TILLUFTSDON, SWEGON, WISE COLIBRI.
TILLUFTSDON, SWEGON EAGLE-ALSD.
FRÄNLUFTSDON, SWEGON EXCA.
FRÄNLUFTSDON, SWEGON PELICAN CE HFA-F.
OVERLUFTSDON, SWEGON SOTTO 125-160, HÅL 160.
OVERLUFTSDON, REC INDOVENT, RW45-TT-160.
RENSLUCKA FÖR CIRKULÄRA KANALER. Se allmänt.
RENSLUCKA FÖR REKTANGULÄRA KANALER. Se allmänt.
KOMBIHUV, BEVENT RASCH, DELTA KH-800, INKL. TAKGENOMFÖRING BRTF, EI-60, -ERFÖRDELIGA TILLBEHÖRSE PRINCIPKISSI).
LUFTBEHANDLINGSAGGREGAT, SWEGON GOLD F RX, AGGREGATSTORLEK 025 ISE (BILAGA 1).
BEFINTLIGT LUFTBEHANDLINGSAGGREGAT (KONTOR).

ALLMÄNT:

GENOMFÖRNINGAR I VÄGG MED Ljudklass SKA DREVAS OCH TÄTAS MED FOG. ANSLUTNINGAR FOGAS I YTTERSTA LAGRET AV GIPSEN PÅ BÅDA SIDOR.
RENSLUCKOR CIRKULÄRA KANALER DIM 500-250= RENSLUCKA EN DIMENSION MINDRE ÄN KANAL. KANALDIM 200-100= RENSLUCKA SAMMA DIMENSION SOM KANAL.
REKTANGULÄRA KANALER= CIRKULÄR RENSLUCKA DIM 315.

BET

ÄNDRINGEN AVSER

DATUM

SIGN

FÖRFRÅGNINGSUNDERLAG

CIK SJÖGRENSKA

www.norconsult.se

A NORCONSULT AB tel. 010-141 80 00

AK NORCONSULT AB tel. 010-141 80 00

SP A-SPRINKLER tel. 010-141 80 00

K TYRENS

EL AFRY

V ENERWEX tel. 0470-70 51 70

VS HELENIUS

BR BRIAB

UPPDRAG NR 24252

RITAD/KONSTR. AV PS

HANDLÄGGARE PS

DATUM 2025-04-25

ANSVARIG PS

KNIVSTA KOMMUN, SÄRSTA 3:1

HYRESGÄSTANPASSNING

CENTRUM FÖR IDROTT OCH KULTUR



LUFTBEHANDLING, PLAN 3, DEL 11

SKALA A1 1:50

A3 1:100

NUMMER V-57-1-3211

BET

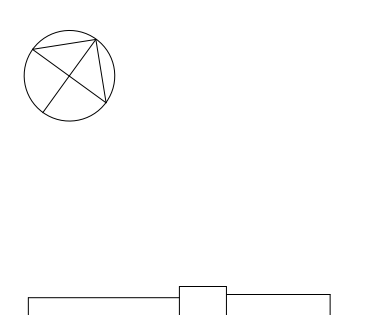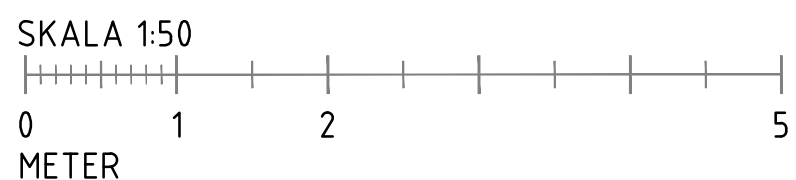

311	312
321	322
331	332
341	342
351	352
361	362
371	372
381	382
391	392
401	402
411	412
421	422
431	432
441	442
451	452
461	462
471	472
481	482
491	492
501	502