


SKALA 1:50
0 1 2 5
METER

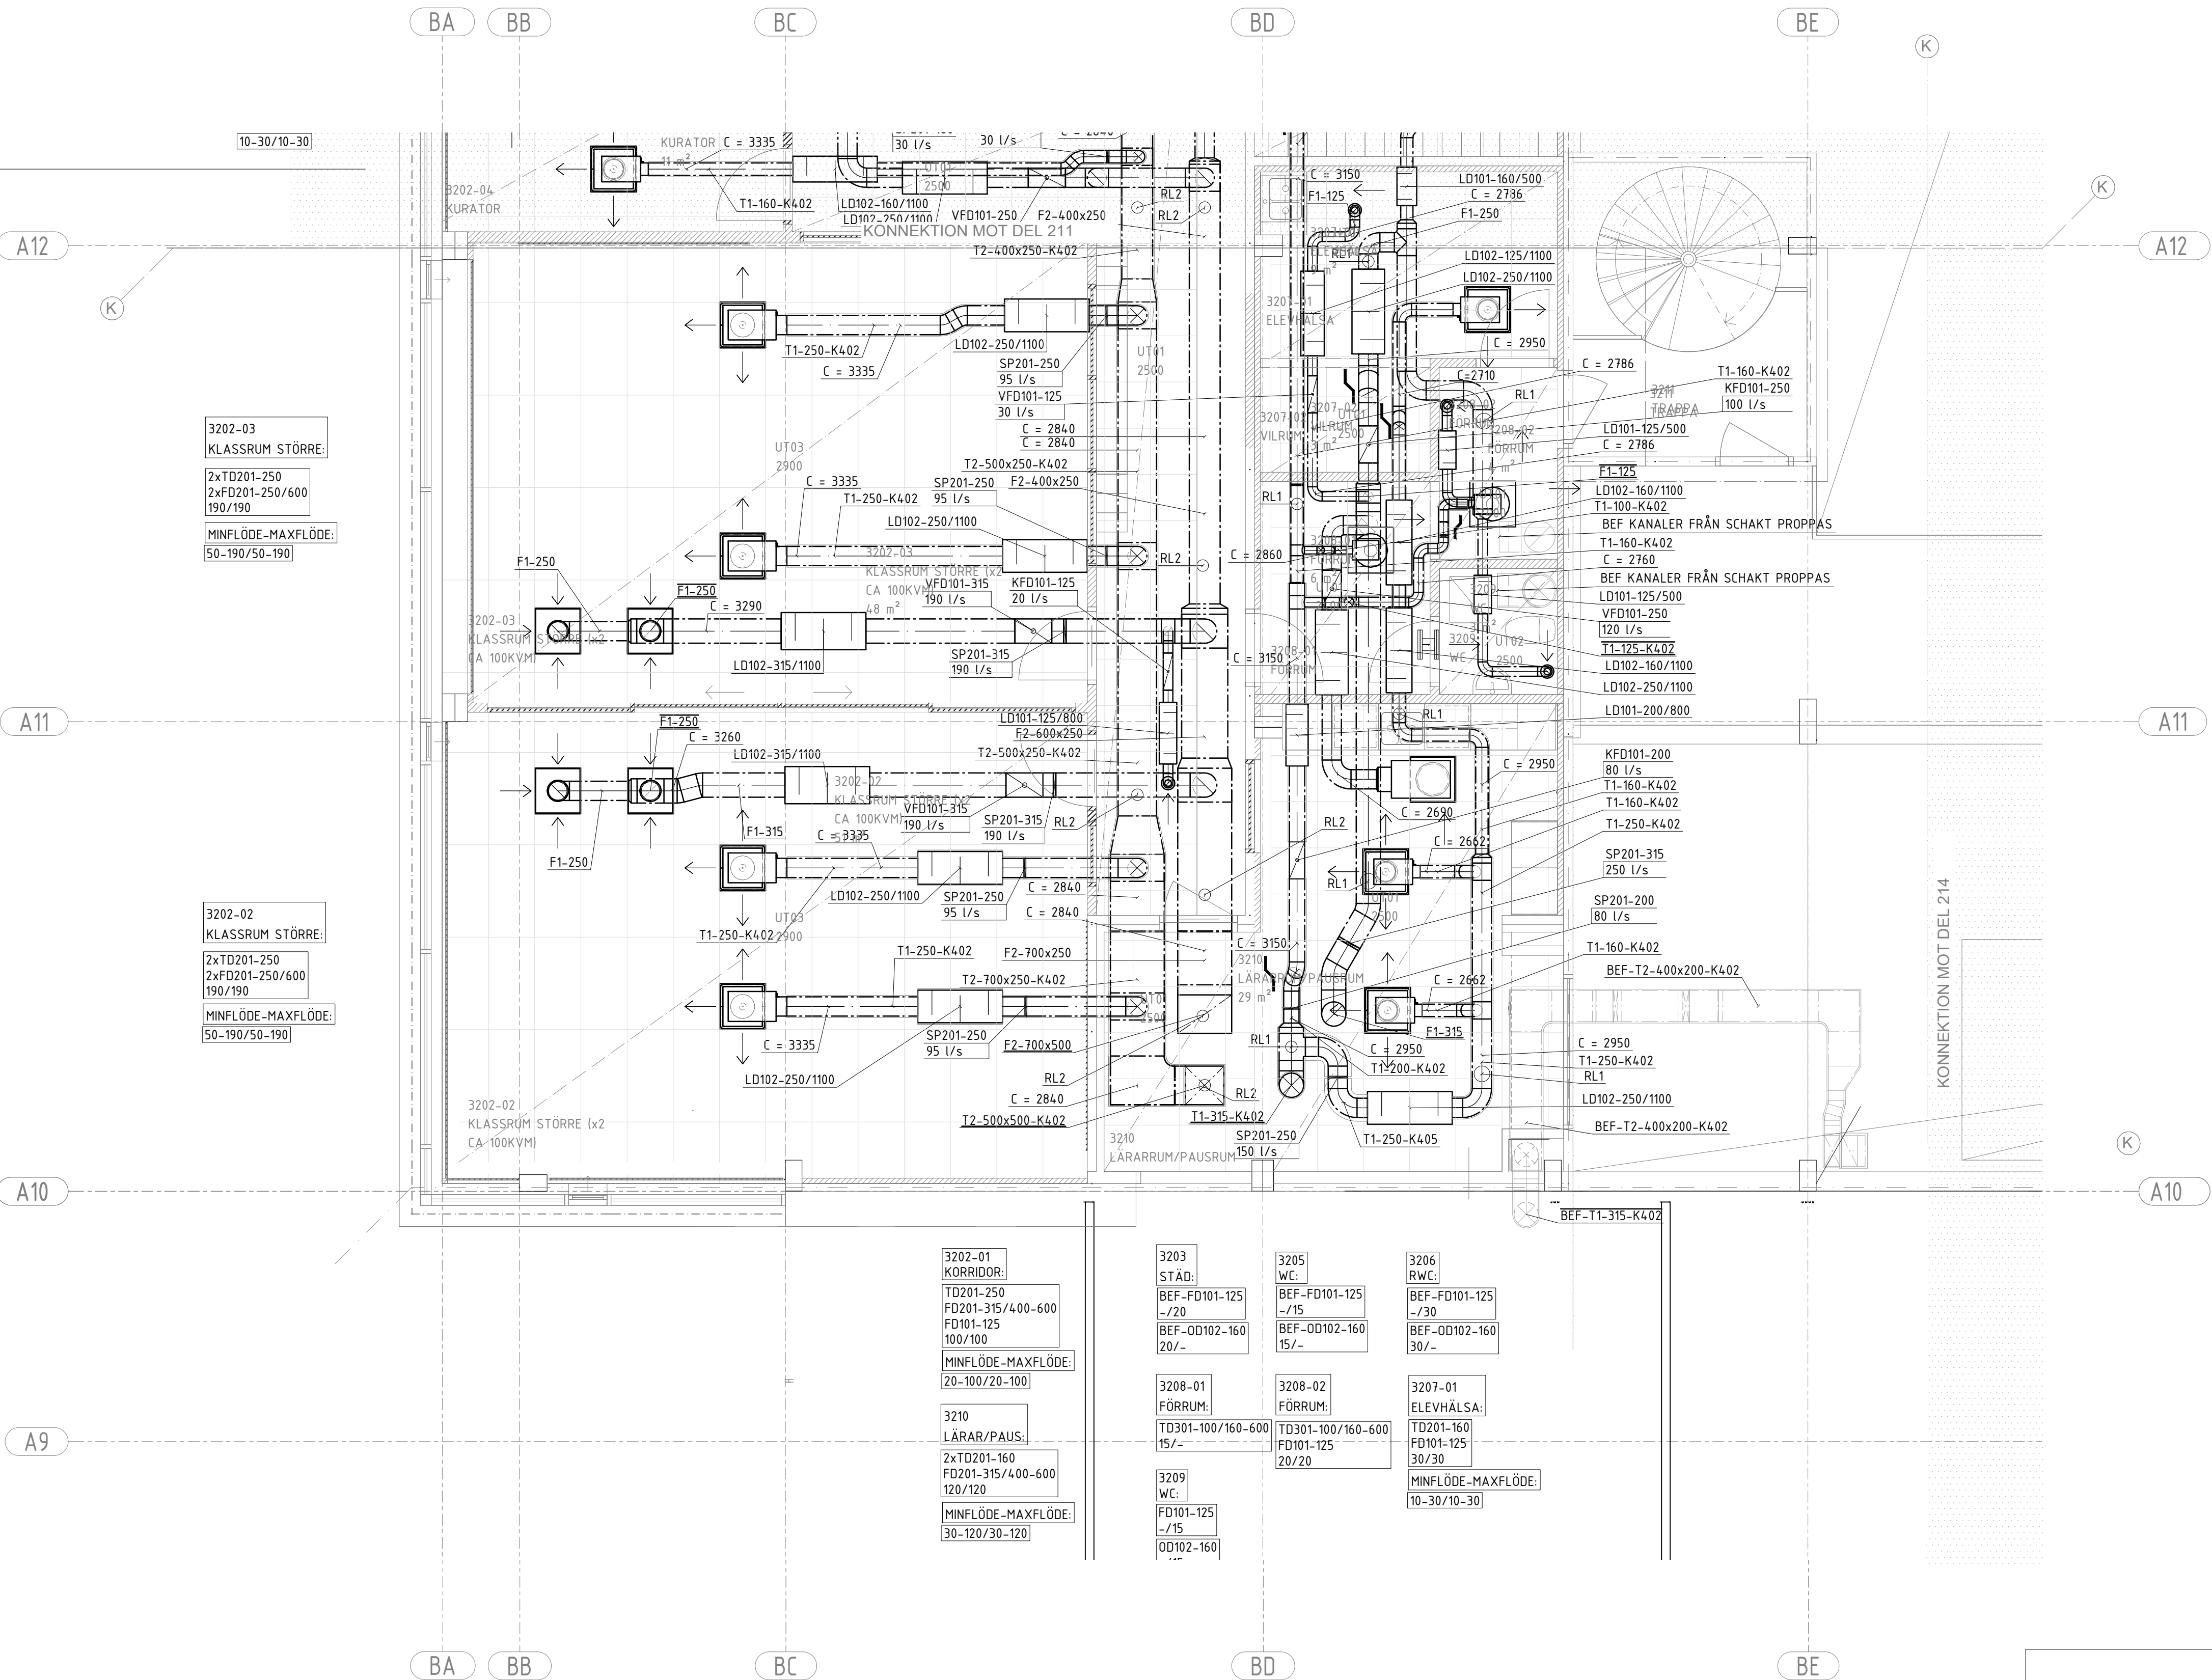

FÖRKLARINGAR

SYSTEM:

T TILLUFT
F FRÅNLUFT
U UTELUFT
A AVLUFT
O ÖVERLUFT

KANALMATERIAL:

1 CIRKULÄRA KANALER, VÄRMFÖRZINKADE
2 REKTANGULÄRA KANALER, VÄRMFÖRZINKADE

ISOLERING:

K402 KONDENSISOLERING, 20 mm
K405 KONDENSISOLERING, 50 mm
V110 VÄRMEISOLERING, 100 mm
B106 BRANDISOLERING, UTV. NÄTMATTA, E160

SAKVAROR:

LD101 CIRKULÄR JUDDÄMPARE, SWEGON SORDO-A E130
LD102 CIRKULÄR JUDDÄMPARE MED BAFFEL, SWEGON SORDO-C E160
LD201 REKTANGULÄR JUDDÄMPARE, SWEGON CADENZA
SP201 IRISSPJÄLL
VFD101 VARIABELFLODESÖN, CIRKULÄRT, SWEGON, WISE DAMPER
KFD101 KONSTANFLODESÖN, CIRKULÄRT, SWEGON, WISE DAMPER
BBS101 BRAND/BRANDGASSP. CIRK. BEVENT RASCH, BSKC6
BBS102 BRAND/BRANDGASSP. REKT. BEVENT RASCH, BSKC6

TD101 TILLUFTSDÖN, FLAKT WOODS STI-C
TD201 AKTIVT TILLUFTSDÖN, SWEGON, WISE COLIBRI
TD301 TILLUFTSDÖN, SWEGON EAGLE+ALSÖ
FD101 FRÅNLUFTSDÖN, SWEGON EXA
FD201 FRÅNLUFTSDÖN, SWEGON PELICAN CE HFA-F
OD102 ÖVERLUFTSDÖN, SWEGON SOTTO 125-160, HÅL 160
OD103 ÖVERLUFTSDÖN, REC INDOVENT, RW45-TT-160
RL1 RENSLUCKA FÖR CIRKULÄRA KANALER. Se allmänt
RL2 RENSLUCKA FÖR REKTANGULÄRA KANALER. Se allmänt
AUD201 KOMBIHUV. BEVENT RASCH, DELTA KH-800, INKL. TAKGENOMFÖRING BRFF, EI-60, -ERFÖRDELIGA TILLBEHÖRSE PRINCIPSSKISS
LA012 LUFTBEHANDLINGSAGGREGAT, SWEGON GOLD F RX, AGGREGATSTORLEK 025 (SE BILAGA 1)
LA005 BEFINTLIGT LUFTBEHANDLINGSAGGREGAT (KONTORI)

ALLMÄNT:

GENOMFÖRINGAR I VÄGG MED LJUDKLASS SKA DREVAS OCH TÄTAS MED FOG. ANSLUTNINGAR FOGAS I YTTERSTA LAGRET AV GIPSEN PÅ BÅDA SIDOR.
RENSLUCKOR CIRKULÄRA KANALER DIM 500-250= RENSLUCKA EN DIMENSION MINDRE ÄN KANAL. KANALDIM 200-100= RENSLUCKA SAMMA DIMENSION SOM KANAL.
REKTANGULÄRA KANALER= CIRKULÄR RENSLUCKA DIM 315.

BET ÄNDRINGEN AVSER DATUM SIGN

FÖRFRÅGNINGSUNDERLAG

CIK SJÖGRENSKA

www.norconsult.se

A	NORCONSULT AB	tel. 010-141 80 00
AK	NORCONSULT AB	tel. 010-141 80 00
SP	A-SPRINKLER	tel. 010-141 80 00
K	TYRENS	
EL	AFRY	
☒ V	ENERWEX	tel. 0470-70 51 70
VS	HELENIUS	
BR	BRIAB	

UPPDRAG NR 24252	RITAD/KONSTR. AV PS	HANDLAGGARE PS
DATUM 2025-04-25	ANSVARIG PS	
KNIVSTA KOMMUN, SÄRSTA 3:1 HYRESGÄSTANPASSNING CENTRUM FÖR IDROTT OCH KULTUR		
LUFTBEHANDLING, PLAN 3, DEL 13		
SKALA A1 1:50 A3 1:100	NUMMER V-57-1-3213	BET